



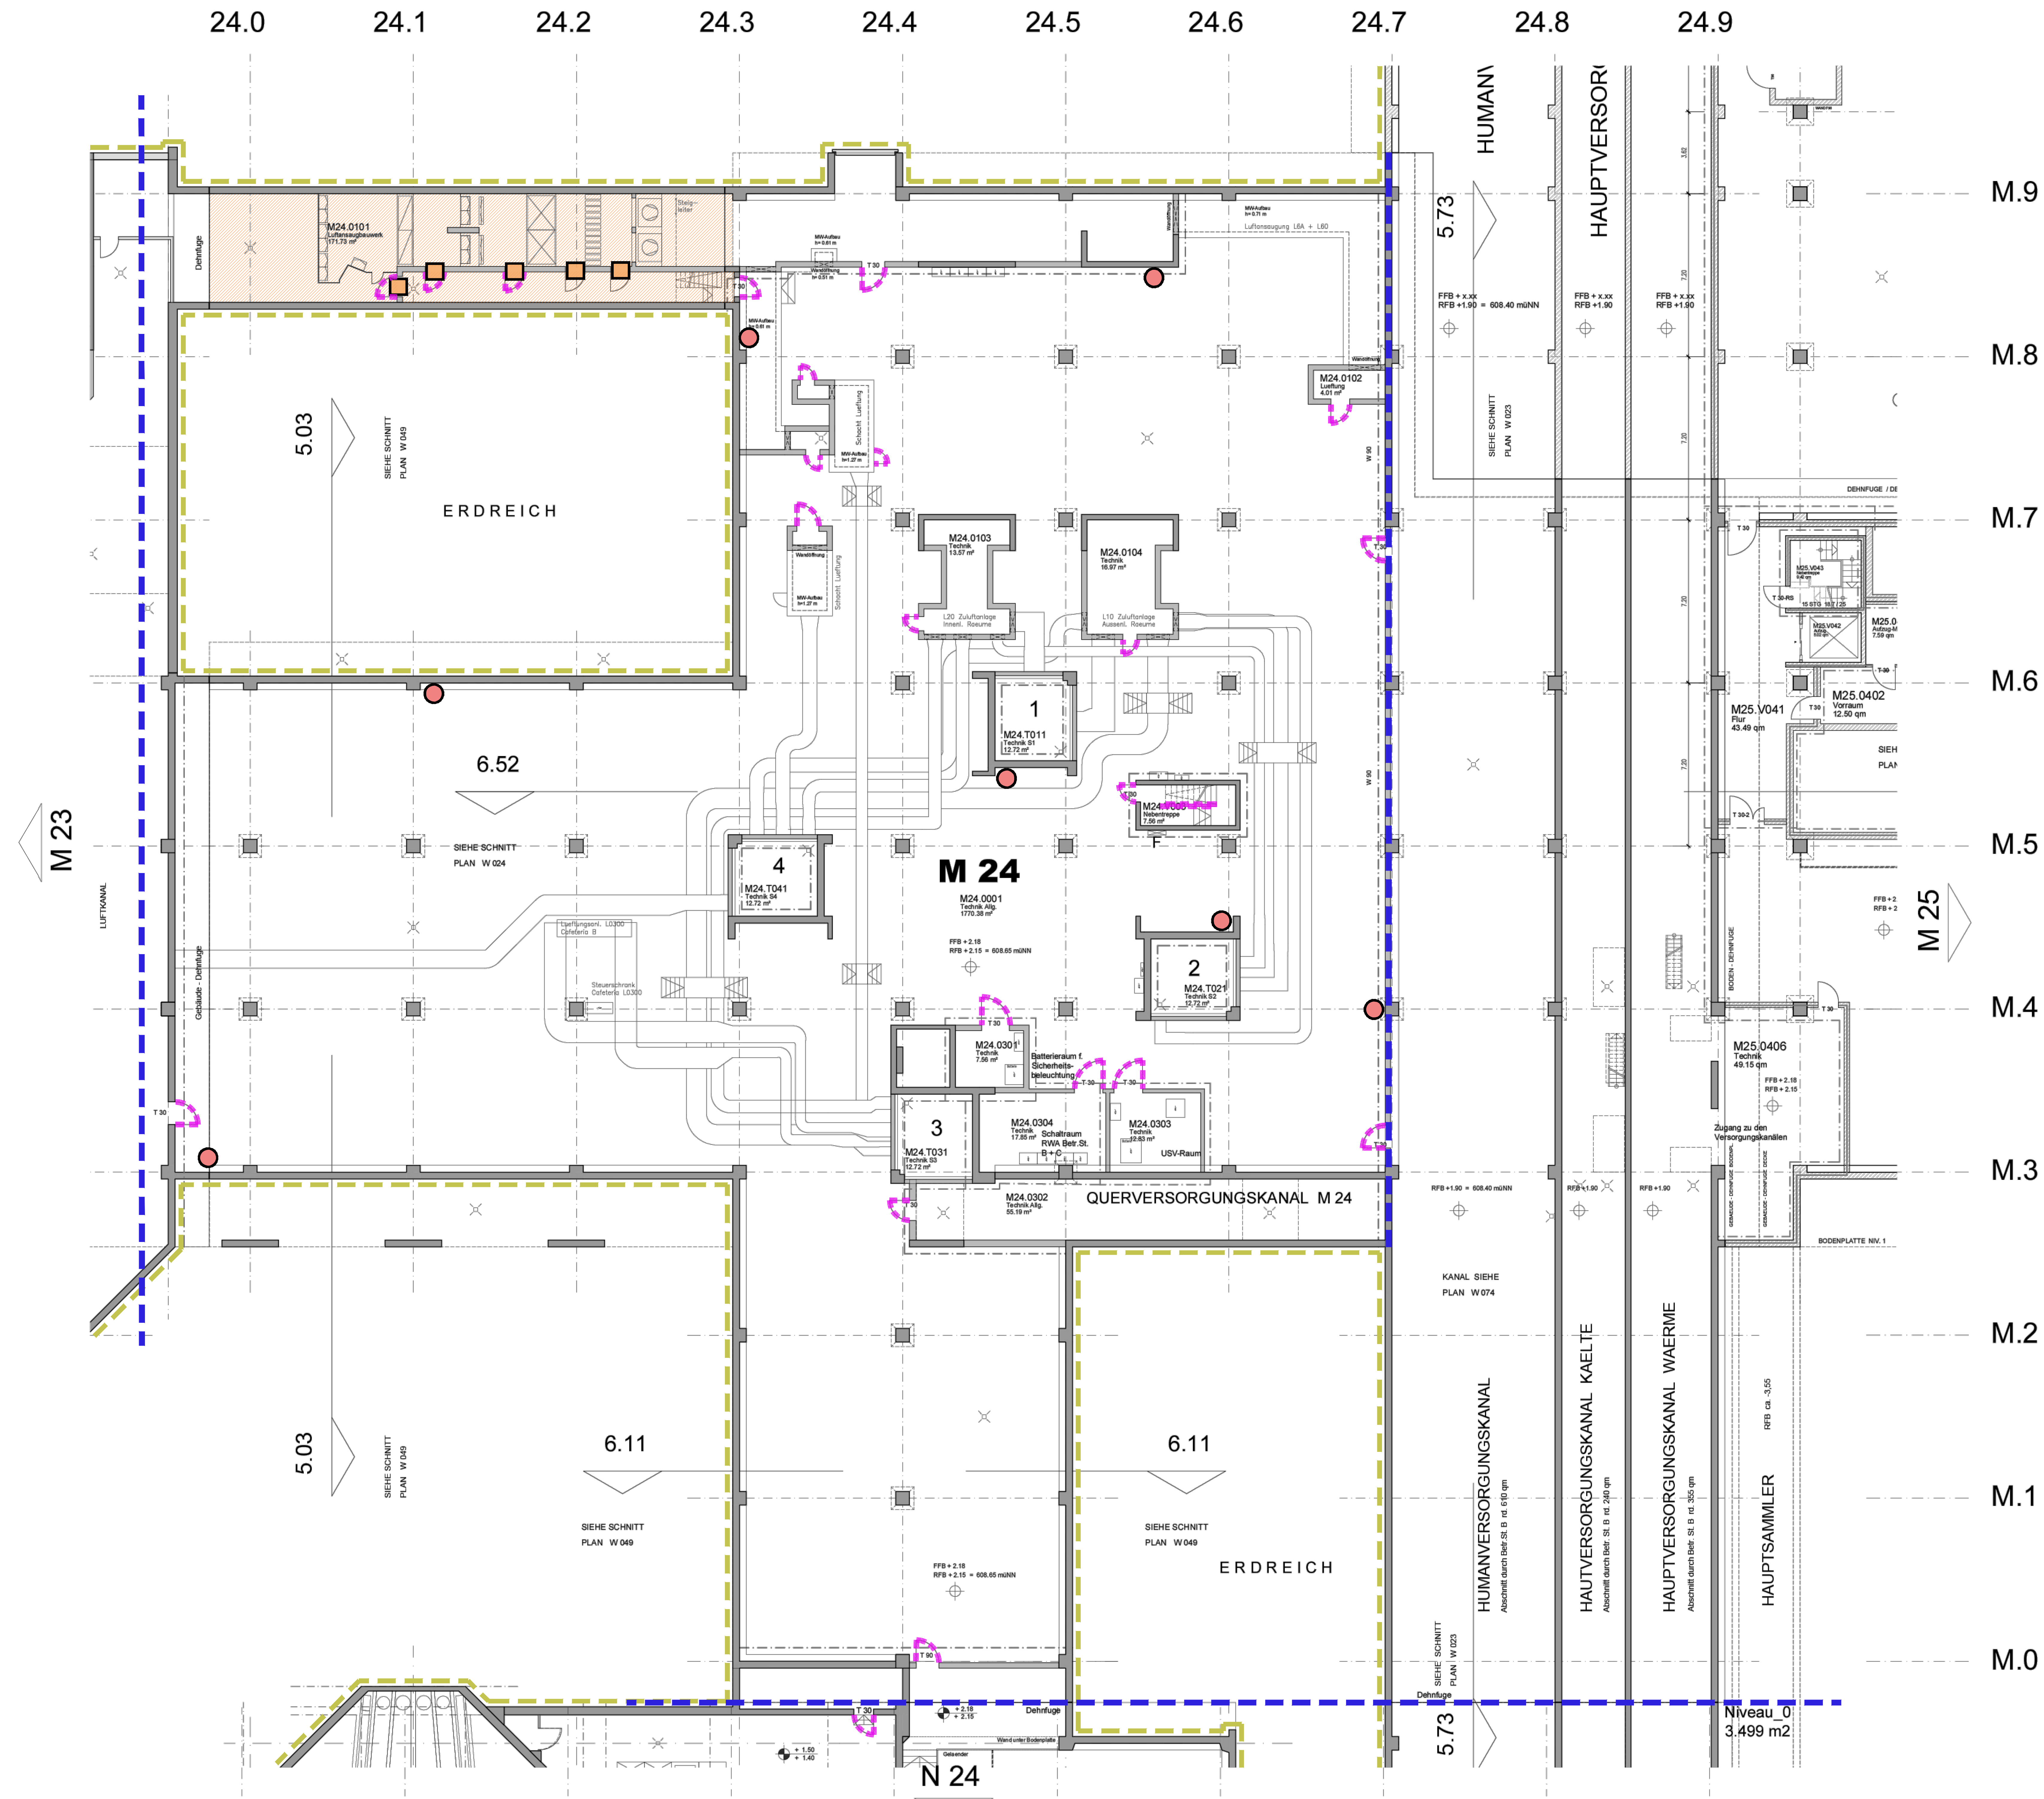

- ## Legende Fundstellen
- | | |
|---|---|
|  | PCB-haltige Fugenmasse zwischen
KS - Wand und Türzarge |
|  | Asbestzement - Steigleitungen |
|  | PCB-haltige Bodenbeschichtung |
|  | Blei-, Chrom - haltige Beschichtung |
|  | PAK - und Asbestverdacht an erdberührenden
Abdichtungen / Beschichtungen von Außenwänden |
|  | Gebäudegrenze |

- Schadstofffundstellen ohne Darstellung im Plan KMF:
 - Isolierung an Rohrleitungen und Lüftungskanälen
- Asbest:
 - Rohrstutzen an Decken-/ Wanddurchbruch
 - Flanschdichtungen an Rohrleitungen
 - Flachdichtungen an Lüftungskanälen
 - Brandschutzklappen (Klappenblatt, Anschlagdichtung)
 - Asbestzement - Rohrleitungen (horizontal)


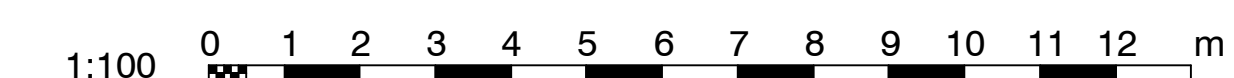


Alle Maße sind am Bau verantwortlich zu überprüfen!


Index	Datum	Änderungsbeschreibung	Bearbeiter

Auftraggeber	Planung MCO Planung GmbH Eschbacher Weg 21 73734 Esslingen Tel: 0711 633230-0 Fax: 0711 633230-50 E-Mail: mcoes@mcp-planung.de	 MCO-Nr. 23943
--------------	--	--

GEBÄUDEÜBERSICHT:

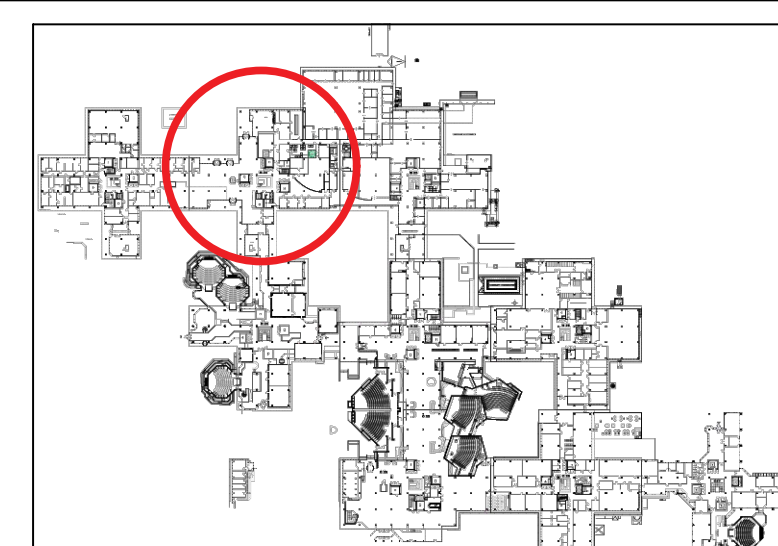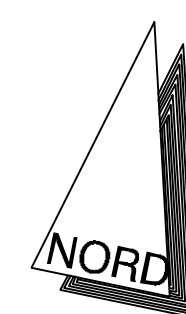

Projekt Nr.:		Bauser:	
SAP-WVE:	SAP-Geb Nr.:	Vermögen und Bau Baden-Württemberg Amt Ulm Mähringer Weg 148 89075 Ulm Tel: 0731 5028800 Fax: 0711/6673-3700 E-Mail: Poststelle.AmtUlm@vbw.bwl.de	
083141	35532000		
Zustellen Geb. Nr.:			
Datenreihe		Projekt	
M24 YU1G G---A00.dwg		Ulm Universität Albert-Einstein-Allee 16 89081 Ulm Maßnahme Schadstoffuntersuchung	
Datenreihe XUSG		Zeichnungsart Gebäudekreuz M 24 Fundstellplan	
Layendaumen/Planende		Grundriss Niv. 0 08.00	
M24 YU1G G-02 008A00			
Planestadium			
09.09.2025		Planzeichnung 1:100	
Merkmal:		Gezeichnet FF	
1:100 Übersichts- u. inn. DIN A0 Verleitet am		Plan gezeichnet Bearbeiter	
		Leiter des Actes/Abteilungs	

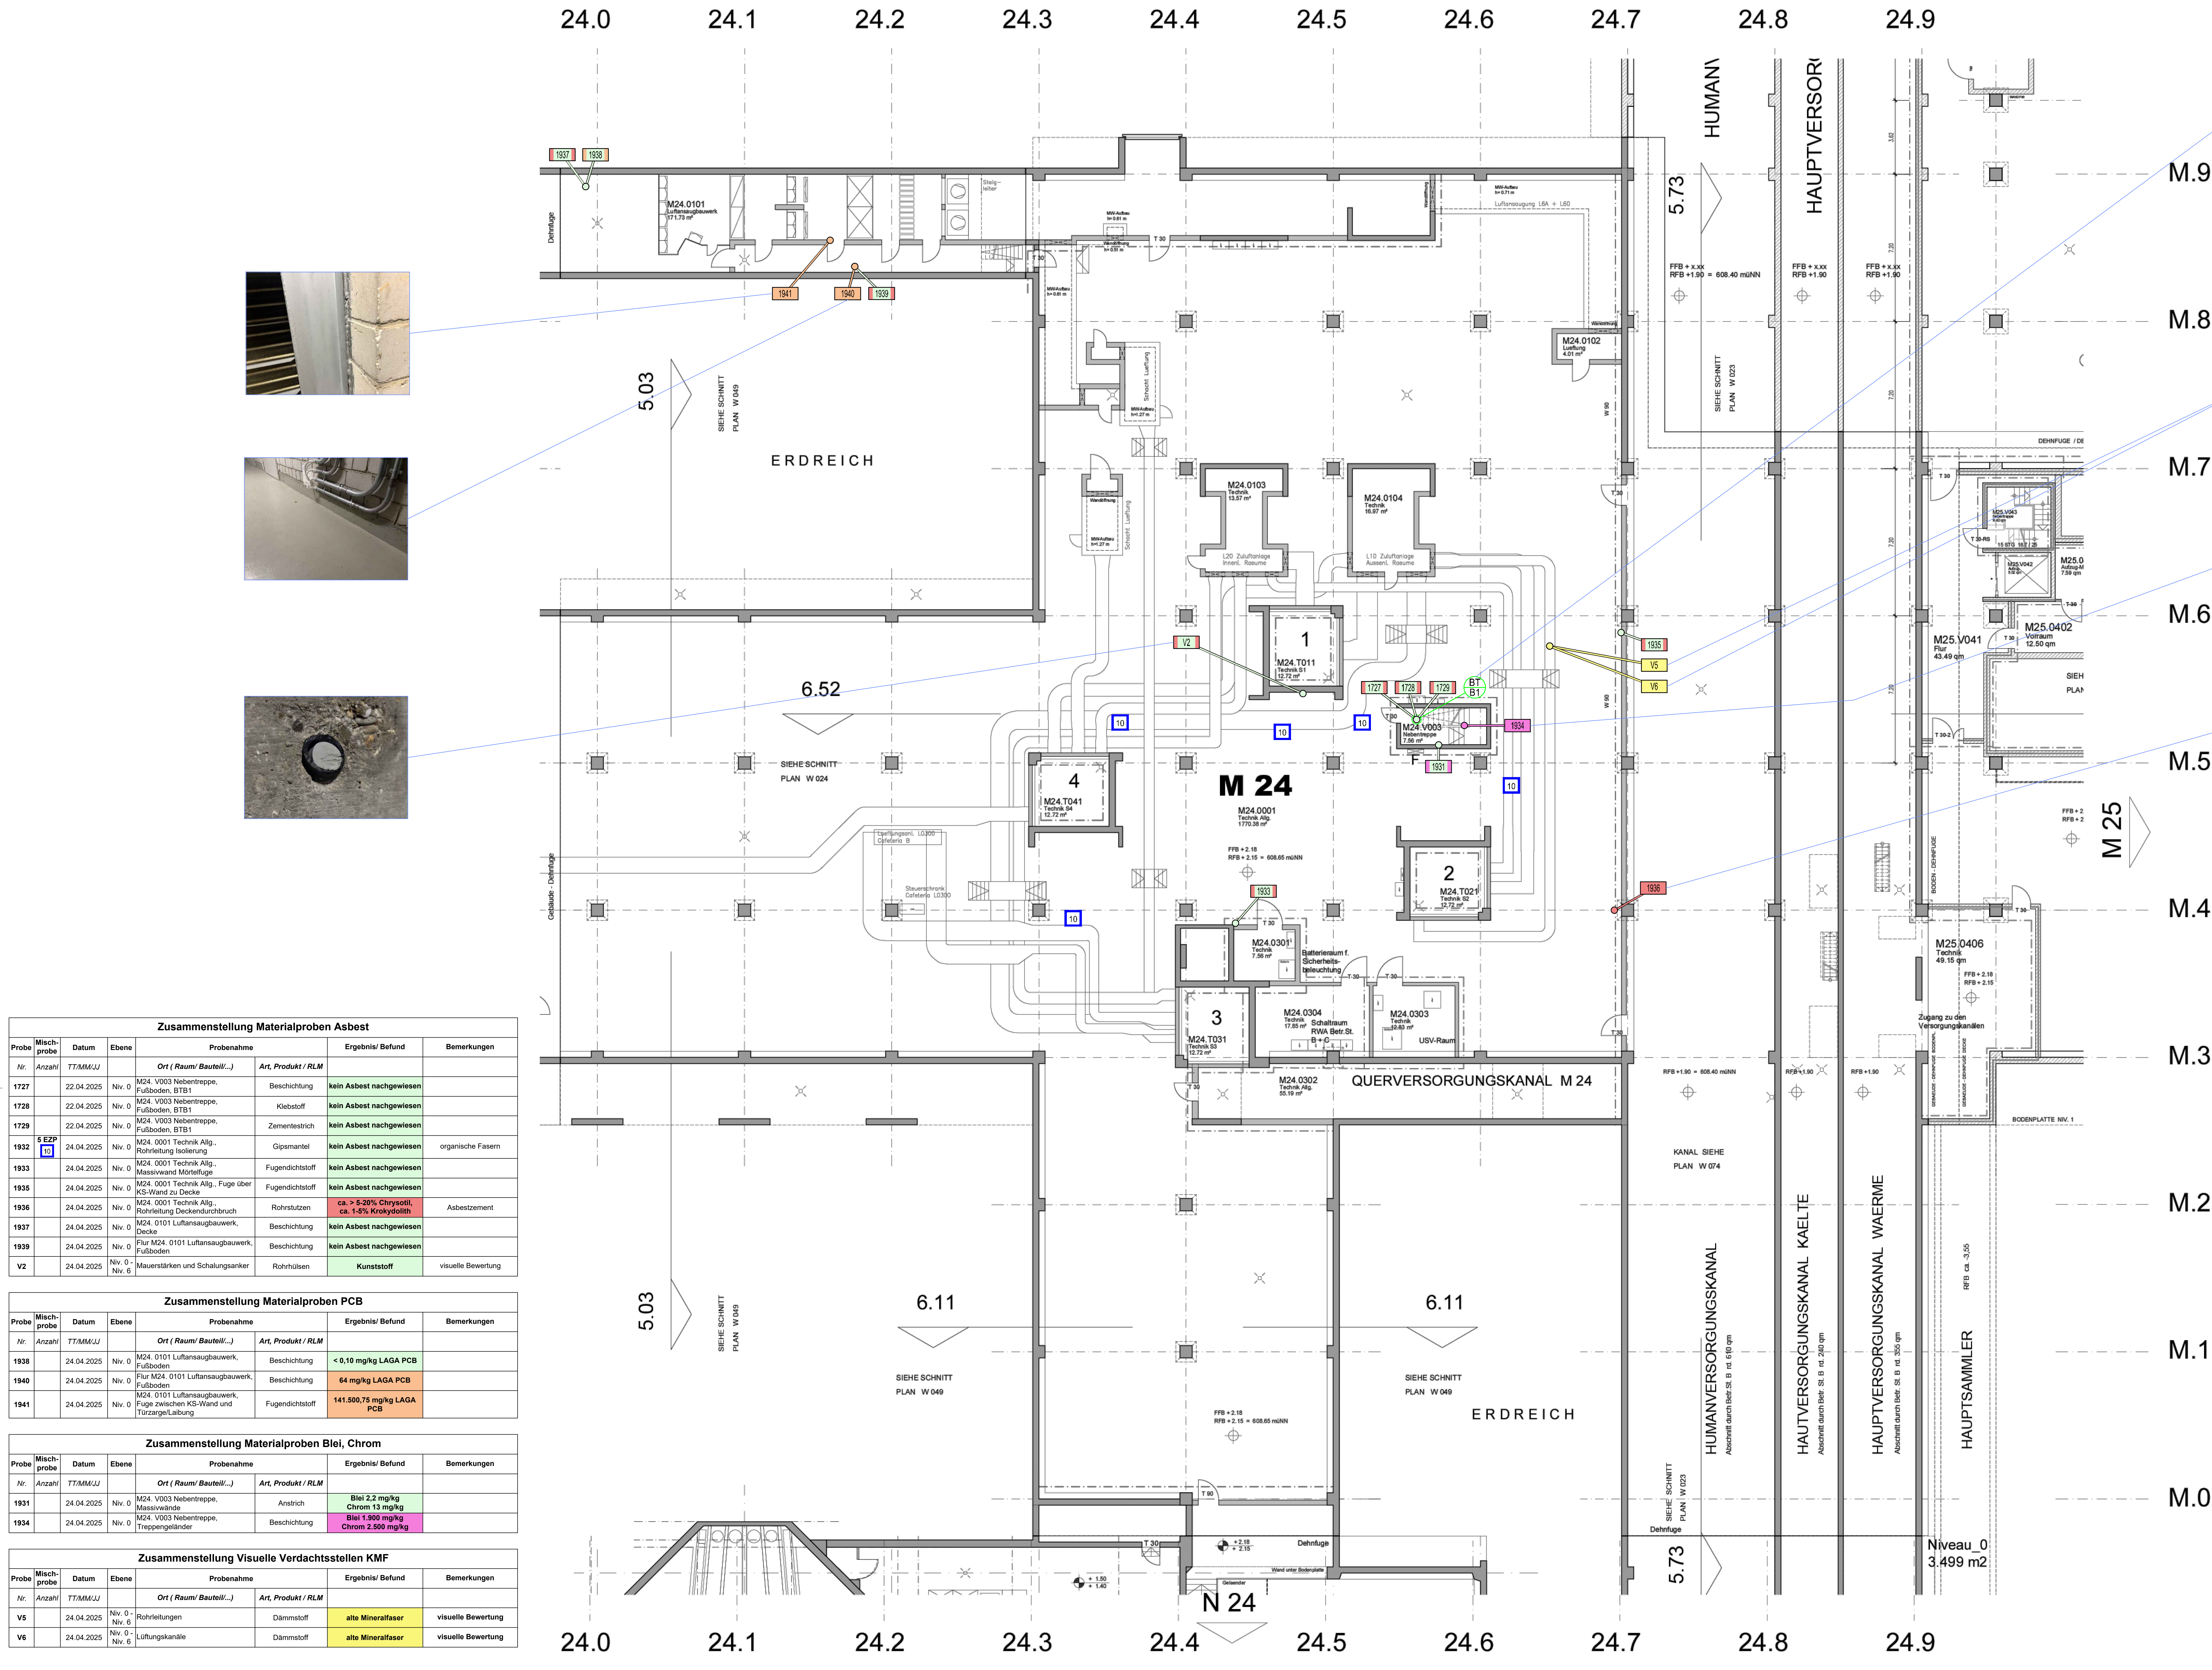

Fußbodenaufbau BT B1, M24.V003, Nebentreppe
Maßstab 1:5

Beschichtung, 1 mm
Probe Asbest (Nr. 1727)
Kleber, 0,5 mm
Probe Asbest (Nr. 1728)
Zementestrich, 38 mm
Probe Asbest (Nr. 1729)
Beton



Legende - Proben

kein Befund mit Befund

Materialprobe: Asbest
Materialprobe: PCB
Materialprobe: Blei, Chrom
Materialprobe: KMF


Bauteilöffnung Nr. x

1:100 0 1 2 3 4 5 6 7 8 9 10 11 12 m

Alle Maße sind am Bau verantwortlich zu überprüfen!

Nr.	Datum	Änderungsbeschreibung	Beststeller

Auftraggeber	Planung
MCO Planung GmbH Eschbacher Weg 21 73734 Esslingen Tel. 0711 633230-0 E-Mail: mco@mco-planung.de	MCO-Nr. 23963

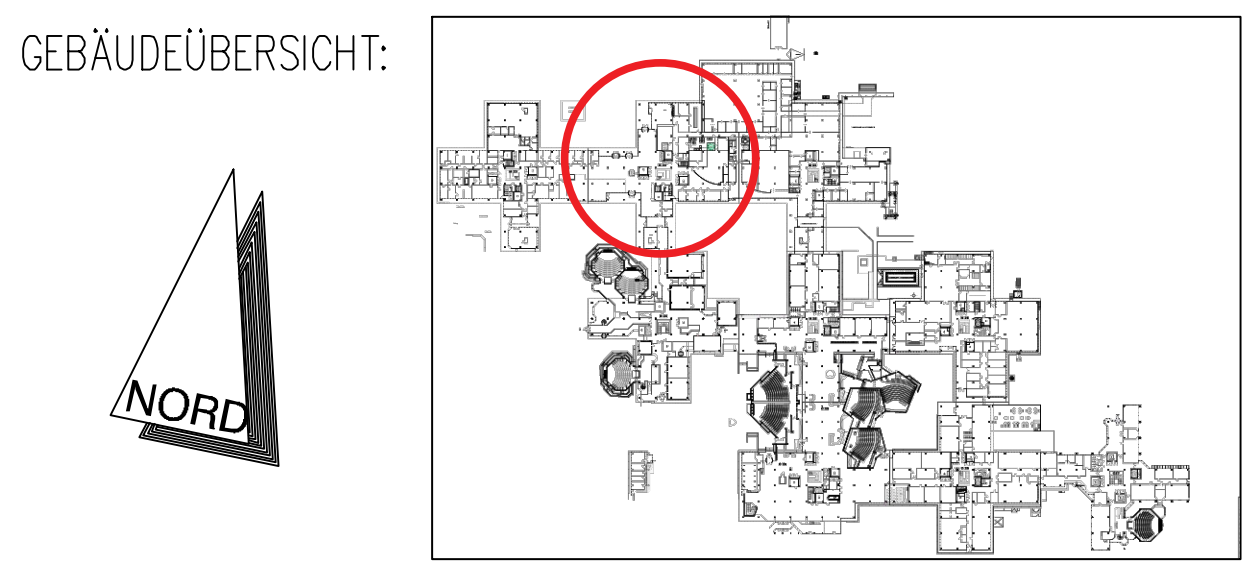

Projekt-Nr. M24_YU1G G-02 001A00 09.09.2025 1:100 1300x841	Bestand Vermögen und Bau Baden-Württemberg Amt Ulm Mähringer Weg 148 89075 Ulm Tel.: 0711 5028800 E-Mail: Poststelle.AmtUL@vbw.bwl.de Fax: 0711/6673-3700 Ulm Universität Albert-Einstein-Allee 16 89081 Ulm Mähringer Schadstoffuntersuchung Gebäudekreuz M 24 Probenahmeplan Grundriss Niv. 0 Plan gezeichnet Leiter des Architektenbüros
--	---