


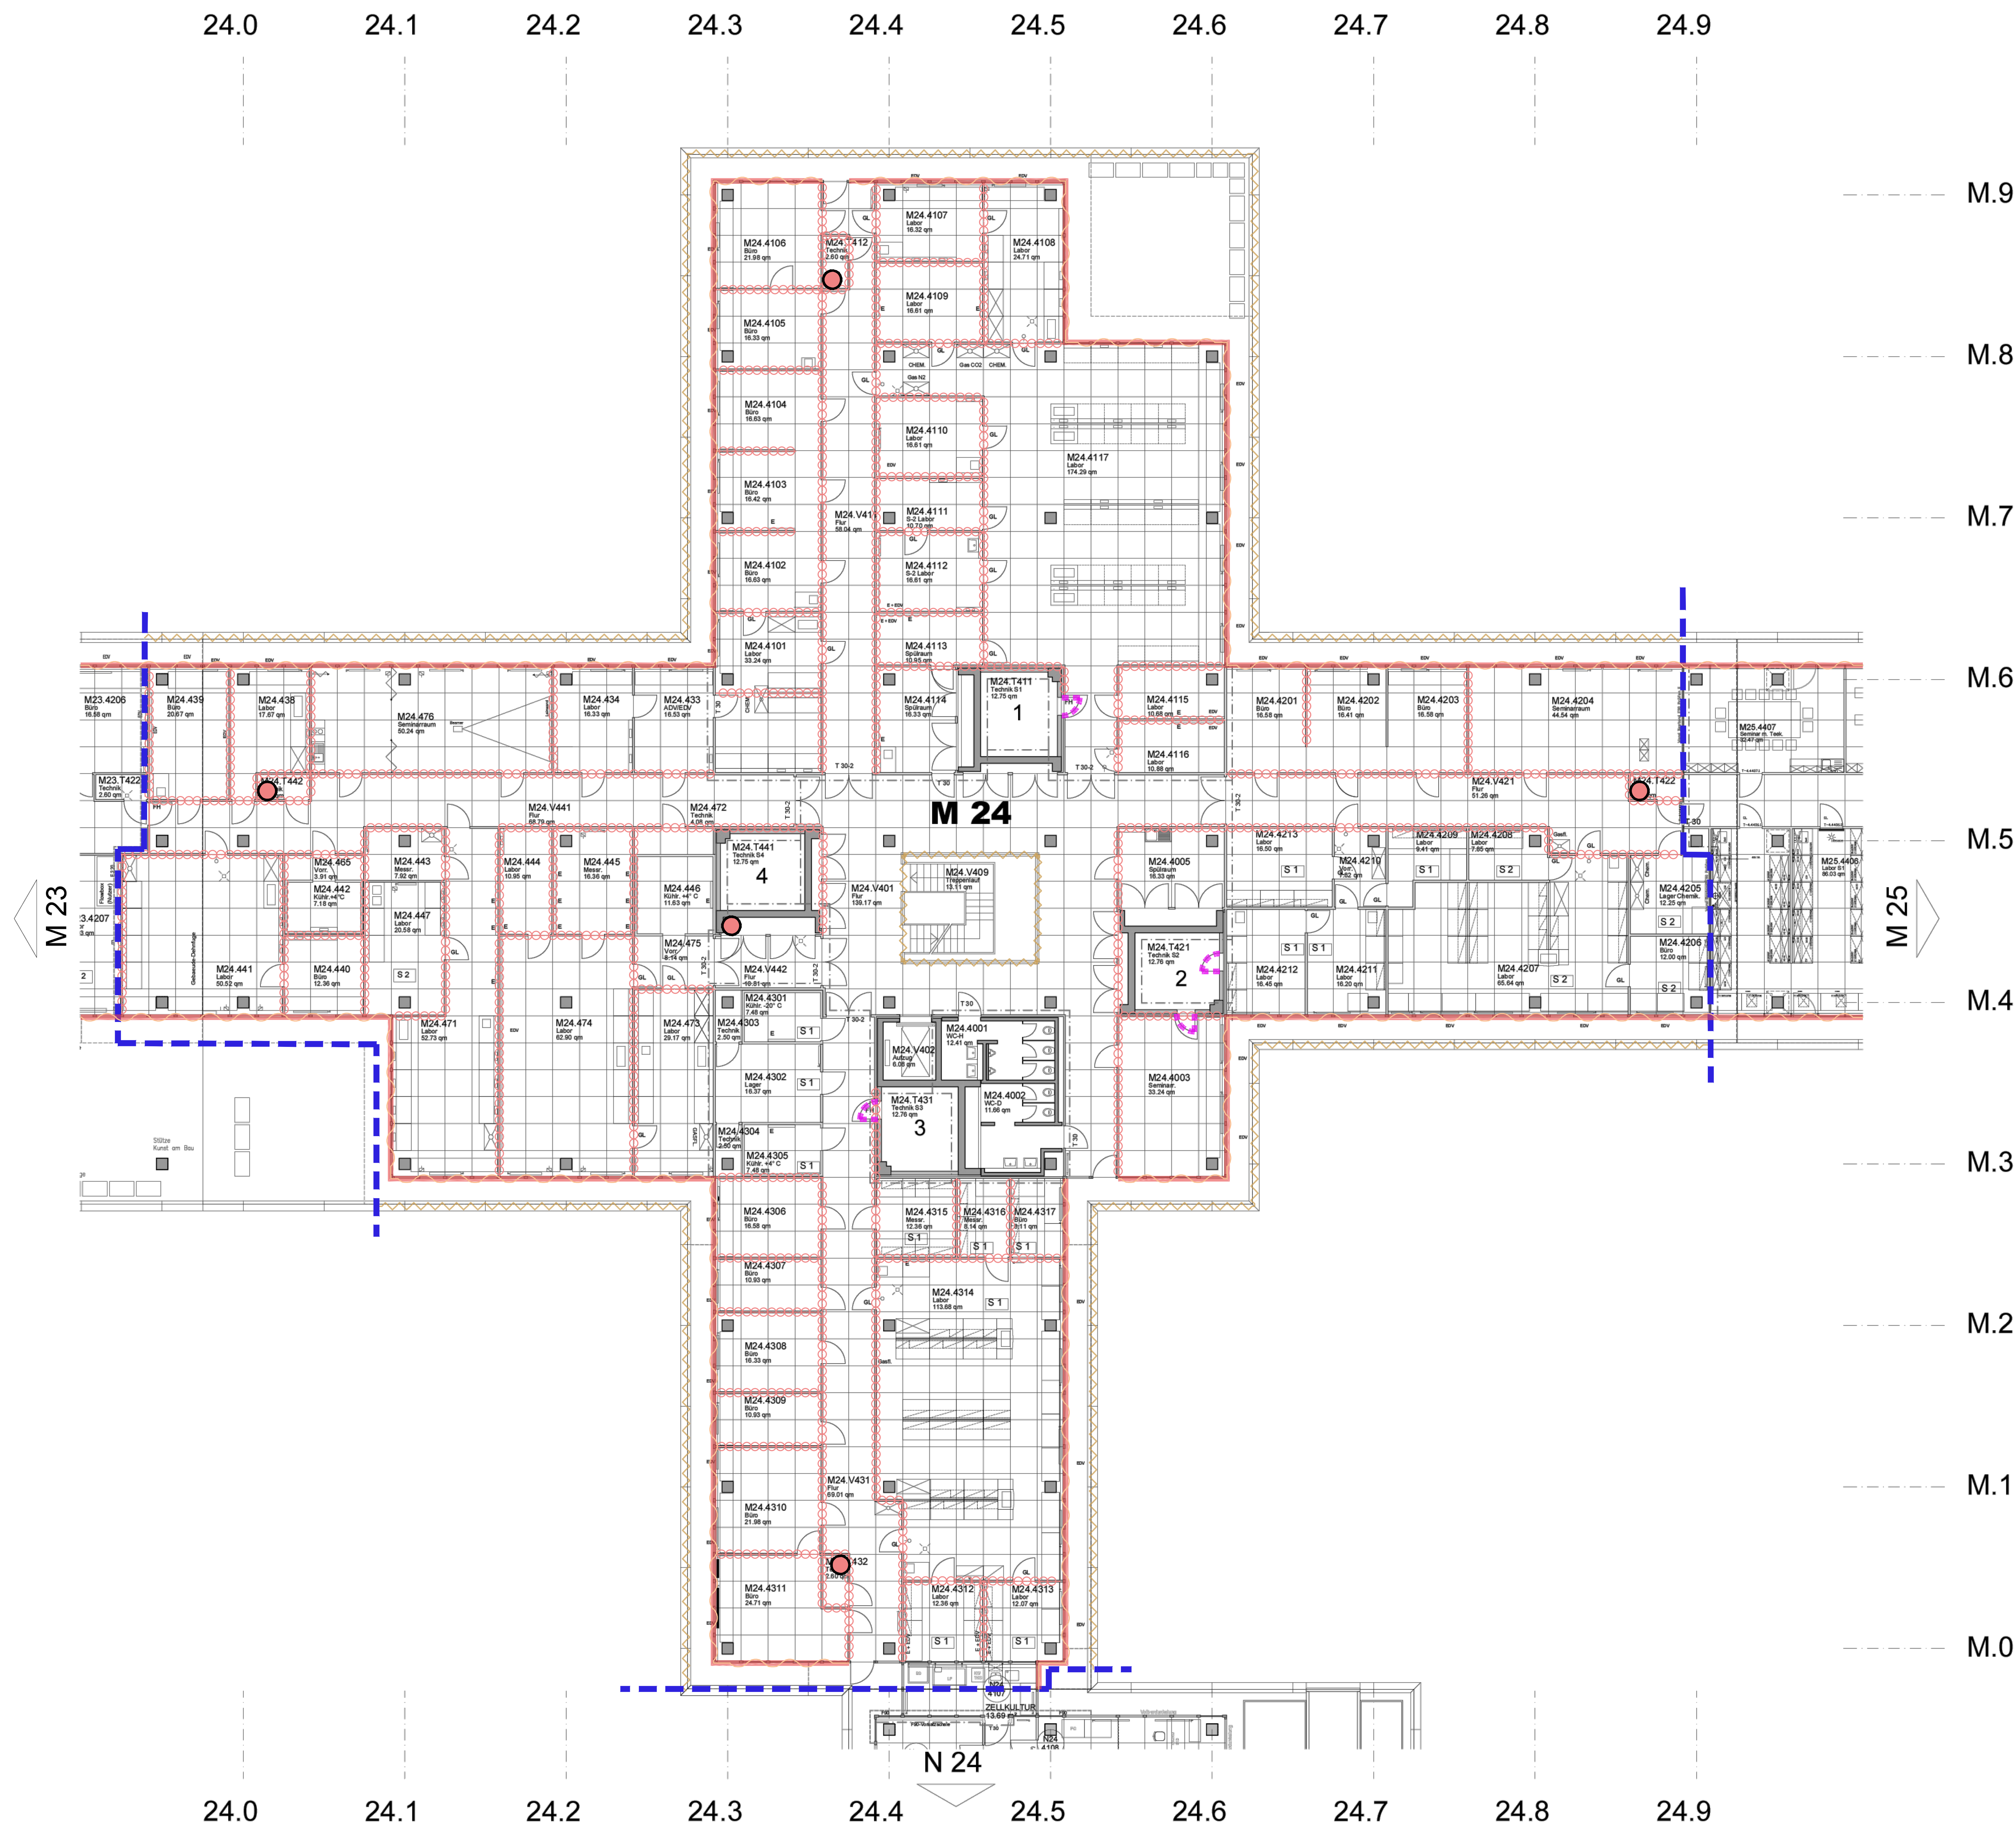


Legende Fundstellen

- | | |
|---|---|
|  | Asbestzement - Steigleitungen |
|  | Asbestzement - Fassadenplatten mit asbesthaltigem Verglasungskitt, KMF - Dämmstoff |
|  | PCB - verunreinigte Fassadenabdeckung |
|  | asbest- und KMF - haltige Mechelwände |
|  | PCB-haltige Fugenmasse im Treppenhaus und am Fluchtbalkon, Sekundärkontamination an Betonfertigteilen |
|  | Gebäudegrenze |

Schadstofffundstellen ohne Darstellung im Plan

KMF:

- Isolierung an Rohrleitungen und Lüftungskanälen
- Asbest:
 - asbesthaltige Flachdichtungen an Heizkörpern
 - Asbestzement - Rohrleitungen (horizontal)
 - Flanschdichtung an Rohrleitungen
 - Flachdichtung an Lüftungskanälen
 - Brandschutzklappen (Klappenblatt, Anschlagdichtung)
- Blei, Chrom:
 - Beschichtung Geländer in Technikschränken


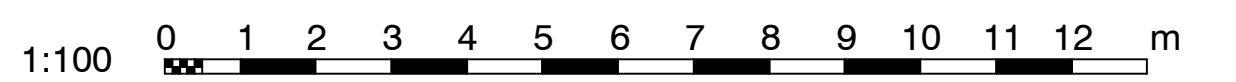


Alle Maße sind am Bau verantwortlich zu überprüfen!

Index	Datum	Änderungsbeschreibung	Bearbeiter

Auftraggeber	Planung MCO Planung GmbH Eschbacher Weg 21 73734 Esslingen Tel: 0711 633230-0 Fax: 0711 633230-50 E-Mail: mcoes@mco-planung.de	 MCO-Nr. 23943
--------------	---	--

GEBÄUDEÜBERSICHT:

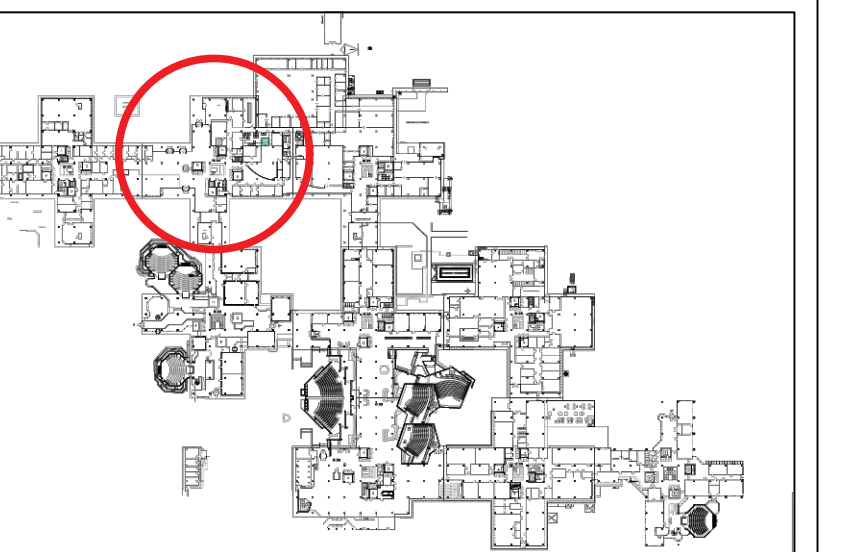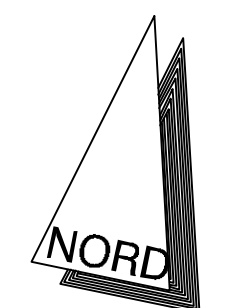

Projekt Nr.: SAP-Name: Drehscheibe: 083141 Nutzer: Geb.-Nr.		Baueinheit: Vermögen und Bau Baden-Württemberg Amt Ulm Mähringer Weg 148 89075 Ulm	
SAP-Geb.-Nr. 35532000		Tel: 0731 5028800 Fax: 0711/66673-3700 E-Mail: Poststelle.AmtUl@vbw.bwl.de	
Extremum: M24 YUIG G---A00.dwg		Project: Ulm Universität Albert-Einstein-Allee 16 89081 Ulm	
Datum: KSEF		Schadstoffuntersuchung	
Lageplanname/Platide:		Flächenbezeichnung	
M24 YUIG G+02 012A00		Gebäudekreuz M 24	
Planungszeit:		Fundstellenplan	
09.09.2025			
Maßstab:			
1:100		Grundriss	
DIN A0		Niv. 4	
Verfasser ein:		Gezeichnet FF	
Prüfer ein:		Plan gezeichnet	
		Leiter des Amtes/Amtsleiter:	

24.0 24.1 24.2 24.3 24.4 24.5 24.6 24.7 24.8 24.9

Zusammenstellung Materialproben PCB						
Probe	Misch-probe	Datum	Ebene	Probenahme	Ergebnis/ Befund	Bemerkungen
Nr.	Anzahl	TT/MM/JJ		Ort (Raum/ Bauteil...)	Art, Produkt / RLM	
1835		22.04.2025	Niv. 4	M24. 4005 Spülraum, Betonstütze	Beschichtung	< 0,10 mg/kg LAGA PCB
1836		22.04.2025	Niv. 4	M24. 4210 Vorr., Fuge Fußboden/Betonstütze	Fugendichtstoff	47,15 mg/kg LAGA PCB
1838		22.04.2025	Niv. 4	M24. 4207 Labor, Trennwand "Mechel", Fuge weiß	Fugendichtstoff	< 0,10 mg/kg LAGA PCB
1839		22.04.2025	Niv. 4	M24. 4207 Labor, Fassade Fuge Fensterelemente Ständerprofile	Fugendichtstoff	< 0,10 mg/kg LAGA PCB
1840		22.04.2025	Niv. 4	M24. 4211 Labor, Fassade Fuge Faserzementplatte	Fugendichtstoff	< 0,10 mg/kg LAGA PCB
1841		22.04.2025	Niv. 4	M24. 4207 Labor, Fassade Fuge Fensterelemente	Fugendichtstoff	10,7 mg/kg LAGA PCB
1842		22.04.2025	Niv. 4	M24. 4207 Labor, Fassade Stoß und unterer Anschluss Kappelste	Fugendichtstoff	8,2 mg/kg LAGA PCB
1844		22.04.2025	Niv. 4	Fluchtbalken vor M24.4207 Labor, Fassade Fuge Balkonbrüstung	Fugendichtstoff	306.600 mg/kg LAGA PCB
1845		22.04.2025	Niv. 4	Fluchtbalken vor M24.4206 Büro, Fassade Fuge Balkonbrüstung	Fugendichtstoff	871,5 mg/kg LAGA PCB
1849		22.04.2025	Niv. 4	M24. 476 Seminarraum, Fuge Fußboden/ Trennwand	Fugendichtstoff	31,35 mg/kg LAGA PCB
1850		22.04.2025	Niv. 4	M24. 476 Seminarraum, Fuge Fußboden/Betonstütze	Fugendichtstoff	39,2mg/kg LAGA PCB
1854		22.04.2025	Niv. 4	M24. V411 Flur, Fußboden	Bodenbelag + Klebstoff	7,15 mg/kg LAGA PCB
1861		22.04.2025	Niv. 4	M24. T432 Technik, Türzarge	Beschichtung	7,1 mg/kg LAGA PCB

Zusammenstellung Materialproben Blei, Chrom						
Probe	Misch-probe	Datum	Ebene	Probenahme	Ergebnis/ Befund	Bemerkungen
Nr.	Anzahl	TT/MM/JJ		Ort (Raum/ Bauteil...)	Art, Produkt / RLM	
1858		22.04.2025	Niv. 4	M24. T432 Technik, Türzarge	Beschichtung	Blei 200 mg/kg Chrom 50 mg/kg



M.9

M.8

M.7

M.6

M.5

M.4

M.3

M.2

M.1

M.0

Legende - Proben


kein Befund	mit Befund	
0000	0000	Materialprobe: Asbest
0000	0000	Materialprobe: PAK
0000	0000	Materialprobe: PCB
0000	0000	Materialprobe: Blei, Chrom
0000	0000	Materialprobe: SCCP
0000	0000	Materialprobe: KMF
BT x		Bauteilöffnung Nr. x

1:100 0 1 2 3 4 5 6 7 8 9 10 11 12 m

Alle Maße sind am Bau verantwortlich zu überprüfen!

Index	Datum	Änderungsbeschreibung	Bearbeiter

Auftraggeber	Planung MCO Planung GmbH Eschbacher Weg 21 73734 Esslingen Tel. 0711 633230-0 E-Mail: mco@mco-planung.de	MCO-Nr. 23943
--------------	---	---------------

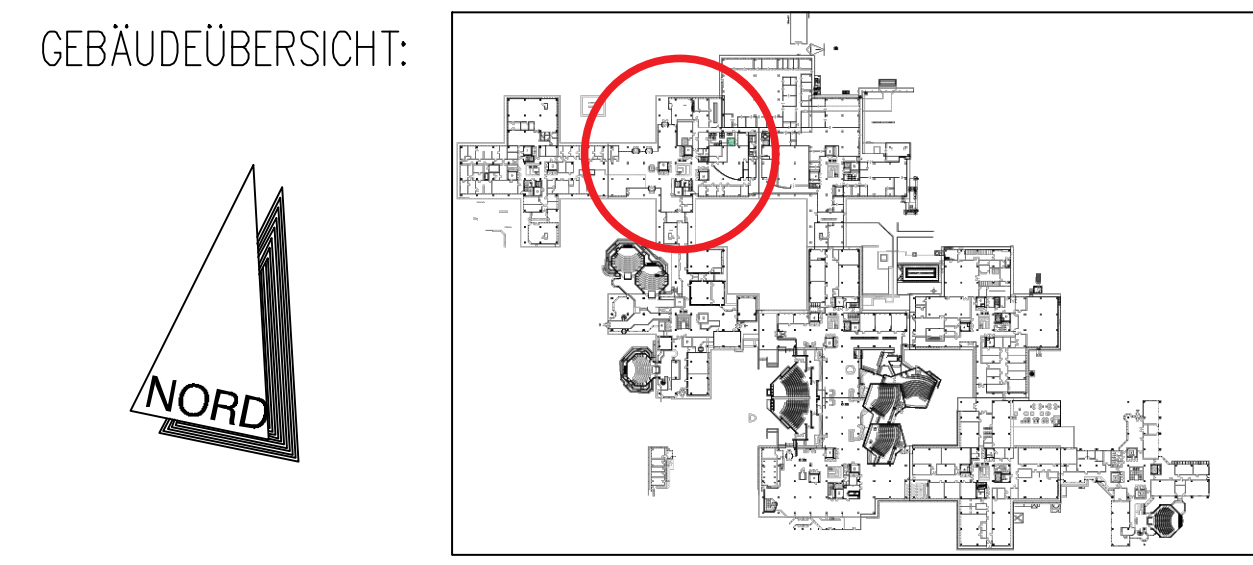

Projekt Nr. Sof-WE 083141	Sof-Ge-Nr. Baureihe 35532000	Bauherr Vermögen und Bau Baden-Württemberg Amt Ulm Mähringer Weg 148 89075 Ulm
Datums M24_YU1G G--- --A00.dwg	Gezeichnet FF	Fax: 0711/6673-3700 E-Mail: Poststelle.AmtUL@vbw.bwl.de
Gezeichnet mhd	Plan gezeichnet	Leiter des Amtes/Abteilung
Lageplan/Profil M24_YU1G G+02 005A00	Grundriss Niv. 4	005-00
Planungsdatum 09.09.2025	Gezeichnet mhd	
Planungsgröße in mm DIN A0	Gezeichnet mhd	