

24.0 24.1 24.2 24.3 24.4 24.5 24.6 24.7 24.8 24.9

Legende Fundstellen

- Asbestzement - Steigleitungen
- Asbestzement - Fassadenplatten mit asbesthaltigem Verglasungskitt, KMF - Dämmstoff
- PCB - haltiger Wandanstrich an Systemwänden (Fremdgutachten)
- PCB - haltiger PVC Bodenbelag (Fremdgutachten)
- PCB - haltige Deckenplatten und Bandraster
- PCB - haltige Beschichtung auf Beton an der Lichtkuppel
- PCB - verunreinigte Fassadenabdeckung
- asbest- und KMF - haltige Mechelwände
- PCB - haltige Fugenmasse im Treppenhaus und am Fluchtbalkon, Sekundärkontamination an Betonfertigteilen
- Gebäudegrenze

Schadstofffundstellen ohne Darstellung im Plan

- KMF:
- Isolierung an Rohrleitungen und Lüftungskanälen
- Asbest:
- asbesthaltige Flachdichtungen an Heizkörpern
 - Asbestzement - Rohrleitungen (horizontal)
 - Flanschdichtung an Rohrleitungen
 - Flachdichtungen an Lüftungskanälen
 - Brandschutzklappen (Klappenblatt, Anschlagsdichtung)
- Blei, Chrom:
- Geländer, Stahlträger in Technischächten

L.0

M.9

M.8

M.7

M.6

M.5

M.4

M.3

M.2

M.1


M.0

1:100 0 1 2 3 4 5 6 7 8 9 10 11 12 m

Alle Maße sind am Bau verantwortlich zu überprüfen!


Index	Datum	Änderungsbeschreibung	Bearbeiter

Auftraggeber	Planung MCO Planung GmbH Eschbacher Weg 21 73734 Esslingen Tel: 0711 633230-0 E-Mail: mco@mco-planung.de	MCO-Nr. 23943
--------------	---	---------------

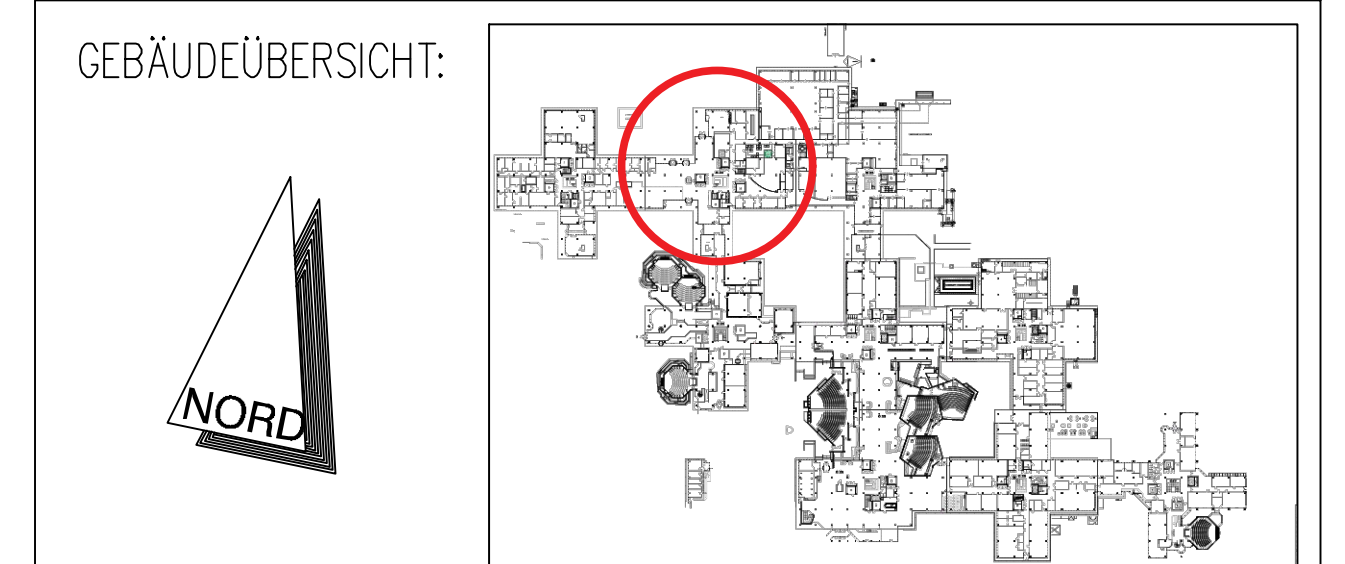

Projekt Nr. SAP-WE 083141	SAP-Obj. Nr. Baureihe 35532000	Bauherr Vermögen und Bau Baden-Württemberg Amt Ulm Mähringer Weg 148 89075 Ulm Tel: 0731 5028800 E-Mail: Poststelle.AmtUL@vbw.bwl.de
Datumsname M24_YU1G G--- A00.dwg	Projet Ulm Universität Albert-Einstein-Allee 16 89081 Ulm	Projet Schadstoffuntersuchung
Legende/Plancode M24_YU1G G+03 013A00	Planungsdatum 09.09.2025	Grundriss Niv. 5
Plangröße in mm DIN A0	Gezeichnet FF	Plan gezeichnet
Verf. am	Beurteiler mhd	Leiter des Amtes/Abteilung

013-00

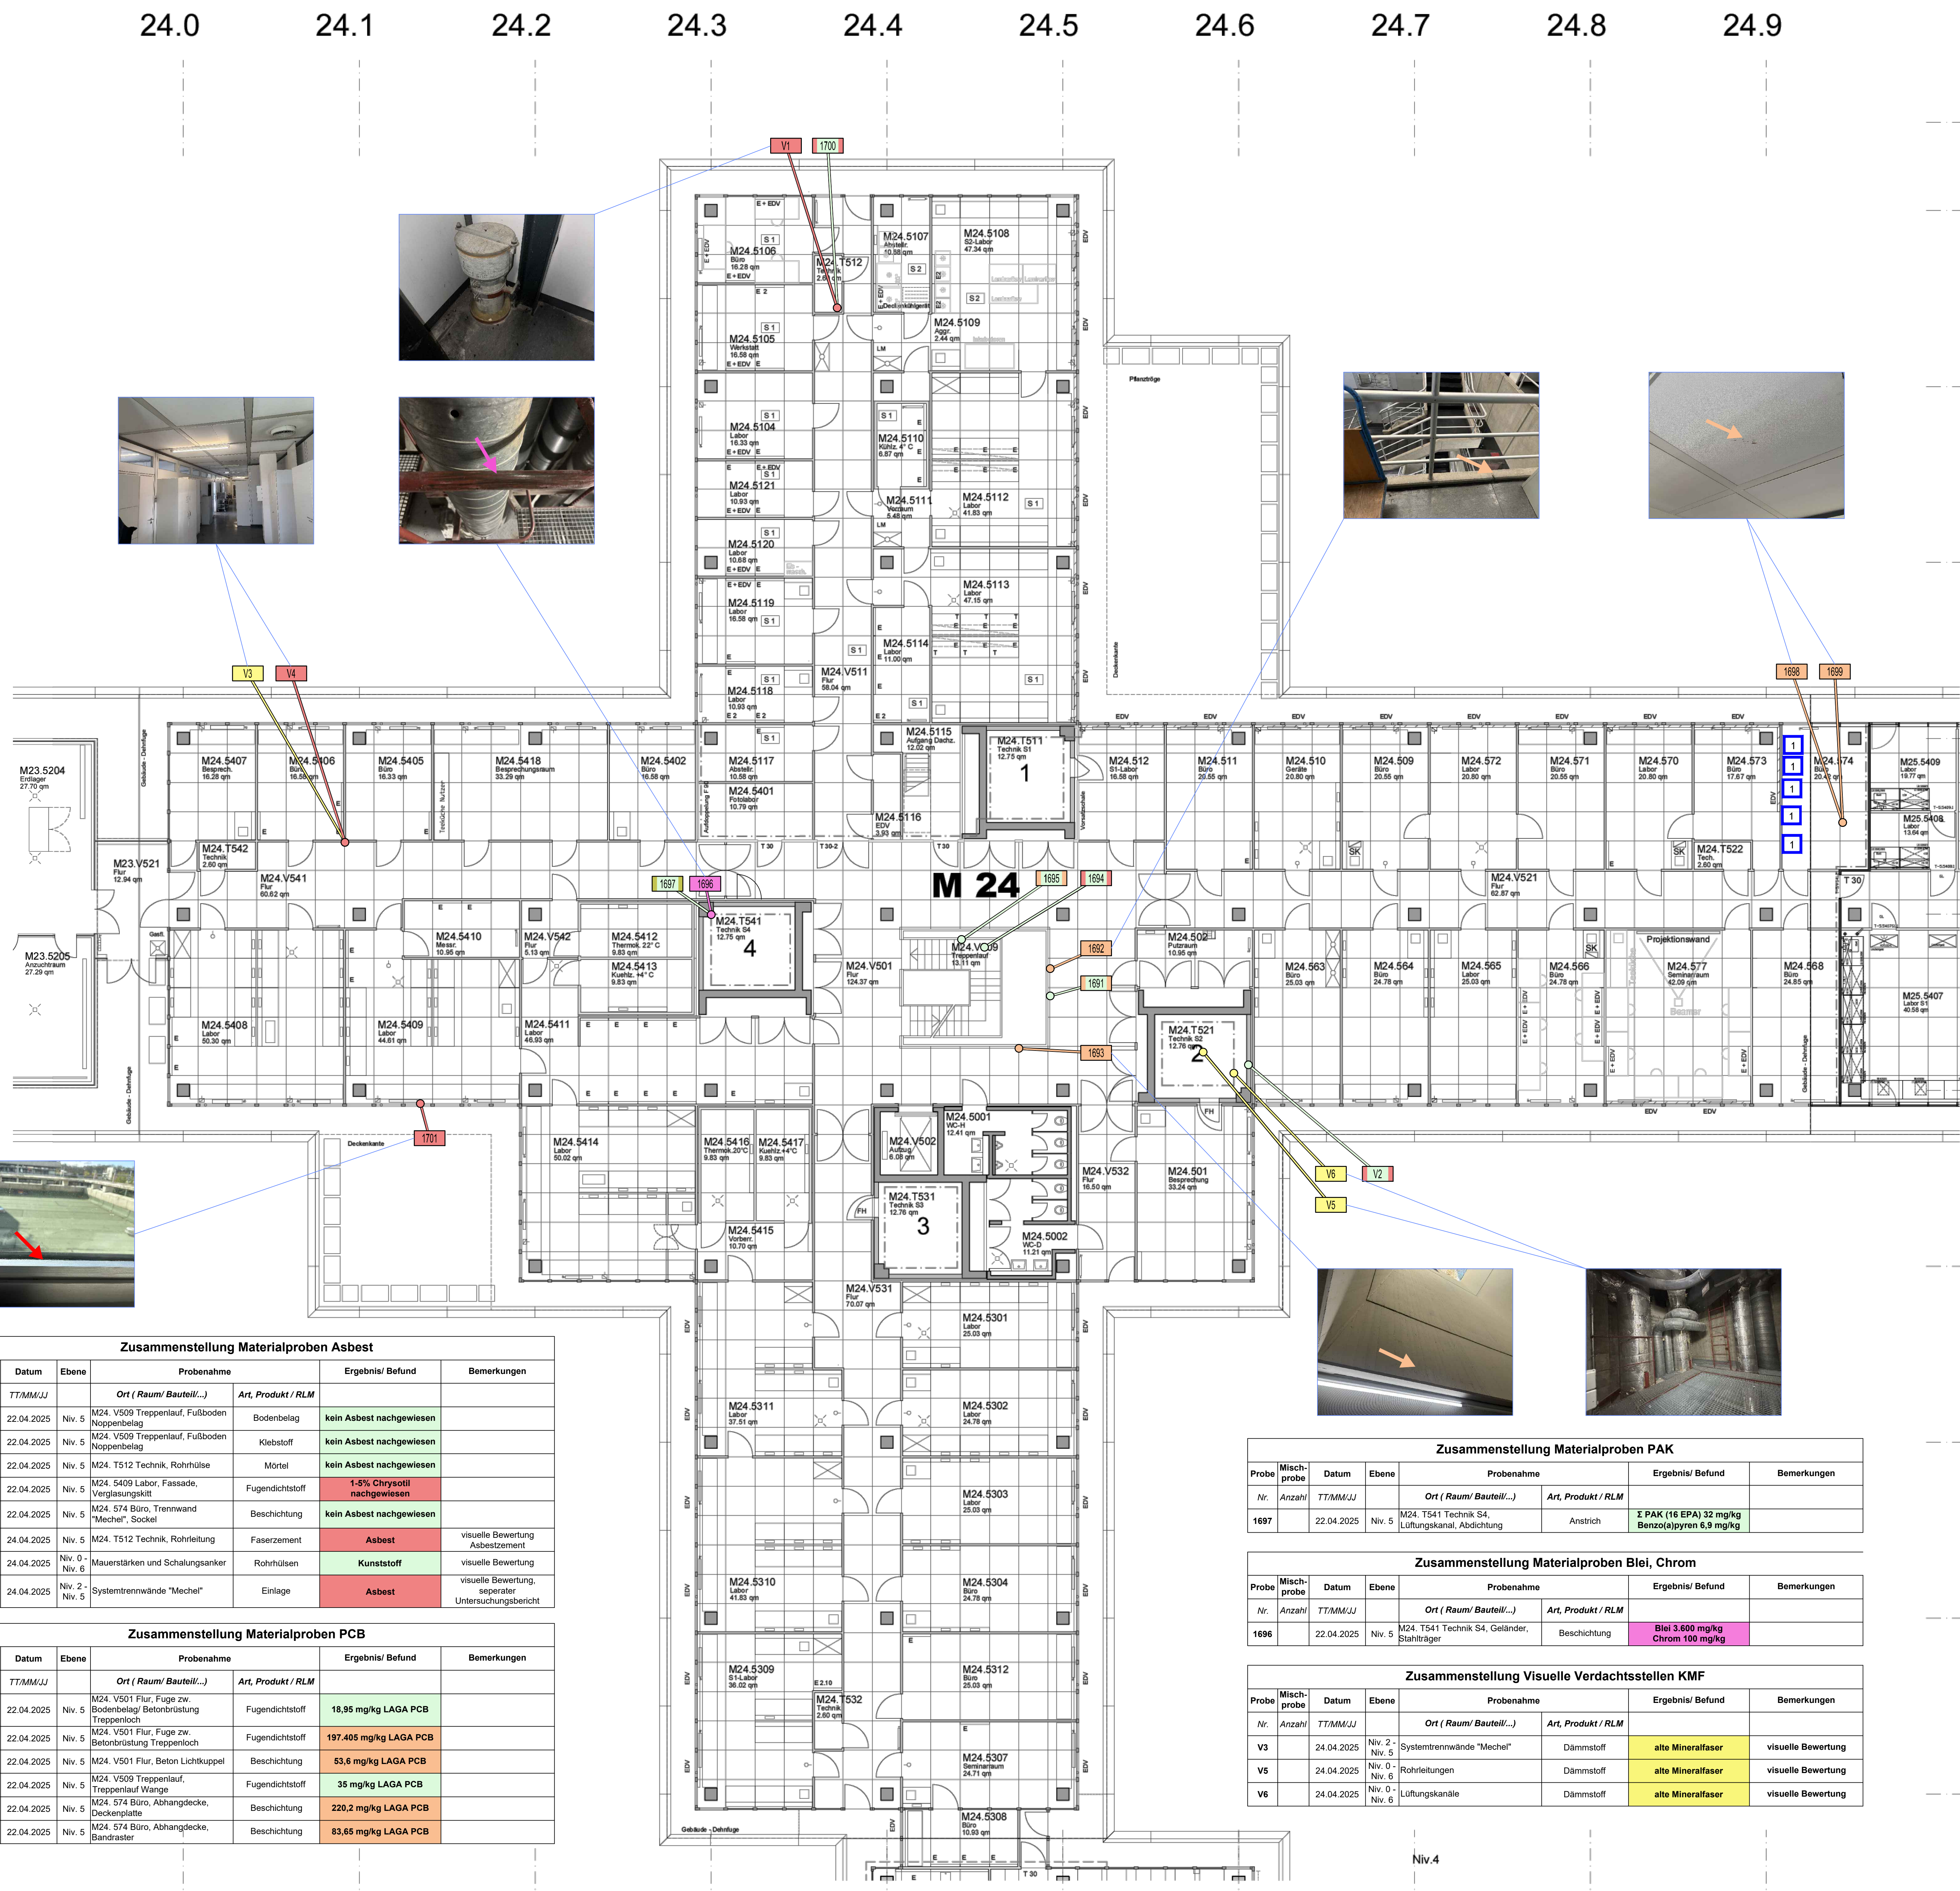


L.0
M.9
M.8
M.7
M.6
M.5
M.4
M.3
M.2
M.1
M.0

Legende - Proben

kein Befund mit Befund


- Materialprobe: Asbest
- Materialprobe: PAK
- Materialprobe: PCB
- Materialprobe: Blei, Chrom
- Materialprobe: KMF
- Bauteilöffnung Nr. x

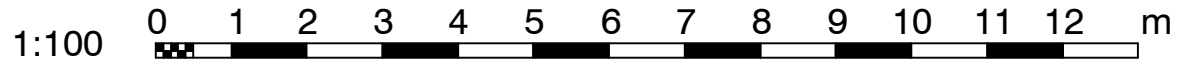

Alle Maße sind am Bau verantwortlich zu überprüfen!

Nr.	Datum	Änderungsbeschreibung	Bearbeiter

Auftraggeber: MCO Planung GmbH
Eschbacher Weg 21
73734 Esslingen
Tel: 0711 633230-0 Fax: 0711 633230-50
E-Mail: mco@mco-planung.de MCO-Nr. 23943

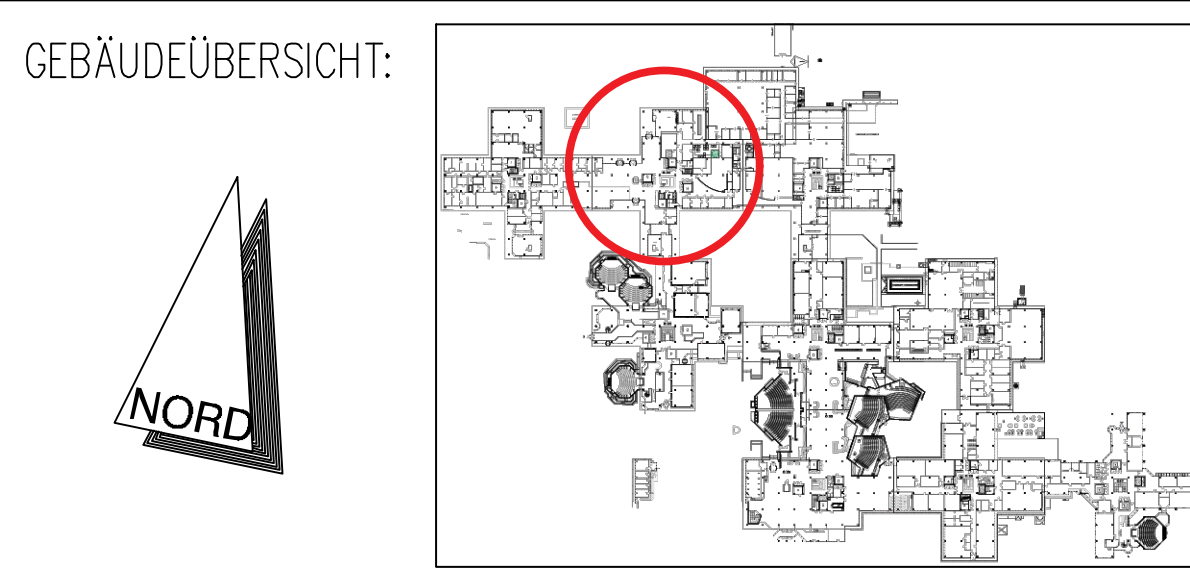

Projekt Nr.: 083141
SAP-WE: 083141
Übernahme: 083141
Bauplan: 35532000
Datum: 09.09.2025
Misch-probe: M24_YU1G G+03 006A00
DIN A0
Verf. am: mhd

Bauherr: **Vermögen und Bau Baden-Württemberg**
Amt Ulm
Mähringer Weg 148
89075 Ulm
Tel: 0731 5028800
Fax: 0711/6673-3700
E-Mail: Poststelle.AmtUL@vbw.bwl.de

Ulm Universität
Albert-Einstein-Allee 16
89081 Ulm
Schadstoffuntersuchung

Grundriss
Niv. 5
006-00

Gezeichnet: mhd
Plan gezeichnet: mhd
Leiter des Amtes/Abteilung: mhd

Zusammenstellung Materialproben Asbest

Probe	Misch-probe	Datum	Ebene	Probenahme	Ergebnis/ Befund	Bemerkungen
Nr.	Anzahl	TT/MM/JJ	Ort (Raum/ Bauteil...)	Art, Produkt / RLM		
1694 A	1	22.04.2025	Niv. 5	M24. V509 Treppenauf, Fußboden Noppenbelag	kein Asbest nachgewiesen	
1694 B	1	22.04.2025	Niv. 5	M24. V509 Treppenauf, Fußboden Noppenbelag	kein Asbest nachgewiesen	
1700	1	22.04.2025	Niv. 5	M24. T512 Technik, Rohrlöse	kein Asbest nachgewiesen	
1701	1	22.04.2025	Niv. 5	M24. 5409 Labor, Fassade, Verglasungsskitt	1-5% Chrysotil nachgewiesen	
1702	1	22.04.2025	Niv. 5	M24. 574 Büro, Trennwand "Mechel", Sockel	kein Asbest nachgewiesen	
V1	1	24.04.2025	Niv. 5	M24. T512 Technik, Rohrleitung	Asbest	visuelle Bewertung Asbestzement
V2	1	24.04.2025	Niv. 5	M24. 574 Büro, Trennwand "Mechel", Sockel	Kunststoff	visuelle Bewertung
V4	1	24.04.2025	Niv. 2	Systemtrennwände "Mechel"	Asbest	visuelle Bewertung, separater Untersuchungsbericht

Zusammenstellung Materialproben PCB

Probe	Misch-probe	Datum	Ebene	Probenahme	Ergebnis/ Befund	Bemerkungen
Nr.	Anzahl	TT/MM/JJ	Ort (Raum/ Bauteil...)	Art, Produkt / RLM		
1691	1	22.04.2025	Niv. 5	M24. V501 Flur, Fuge zw. Bodenbelag/ Betonbrüstung Treppentisch	18,95 mg/kg LAGA PCB	
1692	1	22.04.2025	Niv. 5	M24. V501 Flur, Fuge zw. Bodenbelag/ Betonbrüstung Treppentisch	197.405 mg/kg LAGA PCB	
1693	1	22.04.2025	Niv. 5	M24. V501 Flur, Beton Lichtkuppel	53,6 mg/kg LAGA PCB	
1695	1	22.04.2025	Niv. 5	M24. V509 Treppenauf, Treppenauf Wange	35 mg/kg LAGA PCB	
1698	1	22.04.2025	Niv. 5	M24. 574 Büro, Abhangdecke, Deckenplatte	220,2 mg/kg LAGA PCB	
1699	1	22.04.2025	Niv. 5	M24. 574 Büro, Abhangdecke, Bandstrahler	83,65 mg/kg LAGA PCB	

Zusammenstellung Materialproben PAK

Probe	Misch-probe	Datum	Ebene	Probenahme	Ergebnis/ Befund	Bemerkungen
Nr.	Anzahl	TT/MM/JJ	Ort (Raum/ Bauteil...)	Art, Produkt / RLM		
1697	1	22.04.2025	Niv. 5	M24. T541 Technik S4, Lüftungskanal, Abdichtung	Σ PAK (16 EPA) 32 mg/kg Benzol(a)pyren 6,9 mg/kg	

Zusammenstellung Materialproben Blei, Chrom

Probe	Misch-probe	Datum	Ebene	Probenahme	Ergebnis/ Befund	Bemerkungen
Nr.	Anzahl	TT/MM/JJ	Ort (Raum/ Bauteil...)	Art, Produkt / RLM		
1696	1	22.04.2025	Niv. 5	M24. T541 Technik S4, Geländer, Stahlträger	Blei 3.600 mg/kg Chrom 100 mg/kg	

Zusammenstellung Visuelle Verdachtsstellen KMF

Probe	Misch-probe	Datum	Ebene	Probenahme	Ergebnis/ Befund	Bemerkungen
Nr.	Anzahl	TT/MM/JJ	Ort (Raum/ Bauteil...)	Art, Produkt / RLM		
V3	1	24.04.2025	Niv. 2	Systemtrennwände "Mechel"	alte Mineralfaser	visuelle Bewertung
V5	1	24.04.2025	Niv. 0	Rohrleitungen	alte Mineralfaser	visuelle Bewertung
V6	1	24.04.2025	Niv. 0	Lüftungskanäle	alte Mineralfaser	visuelle Bewertung